

Malkin Farm

Brow Lane

Holmfirth

HD9 2RJ

07946872499

paul@paulmatthewsarchitectural.co.uk

www.paulmatthewsarchitectural.co.uk

Company Registration Number: 09898149 – Company
Registered in England and Wales

Do not scale from drawing, use figured dimensions only.

All dimensions must be checked and verified on site prior to commencement of works and architect to be notified of any discrepancies.

The copyright for these drawings remains the property of Paul MatthewsArchitectural Ltd. They must not be reproduced in any way without prior written consent from the originator (Paul MatthewsArchitecturalLtd).

KEY

- | | |
|---|--|
|  | Smoke alarm ~ mains powered and interconnected |
|  | Heat alarm ~ mains powered and interconnected |
| SG | Safety Glass |
| obs | Obscure Glazing |
| E | Extract Fan |
| F | Flue |
| SVP | Soil & Vent pipe |
| RWP | Rain water pipe |
| B.I.G | Back inlet gully |
| EW | Escape Window |
|  | FD30 Fire door |
|  | Mechanical Extract Fan |

Project

Erection of 2 Attached Dwellings on Land
Adjacent, 2, Hoyle Ing, Linthwaite, Huddersfield,
HD7 5RX.


Client

Walker Good Homes Ltd

Drawing Title/Issue

Building Regulation Stage Section

scale	date	sheet size	dwg. no.
1:50	07/2026	A3	26/1362/04

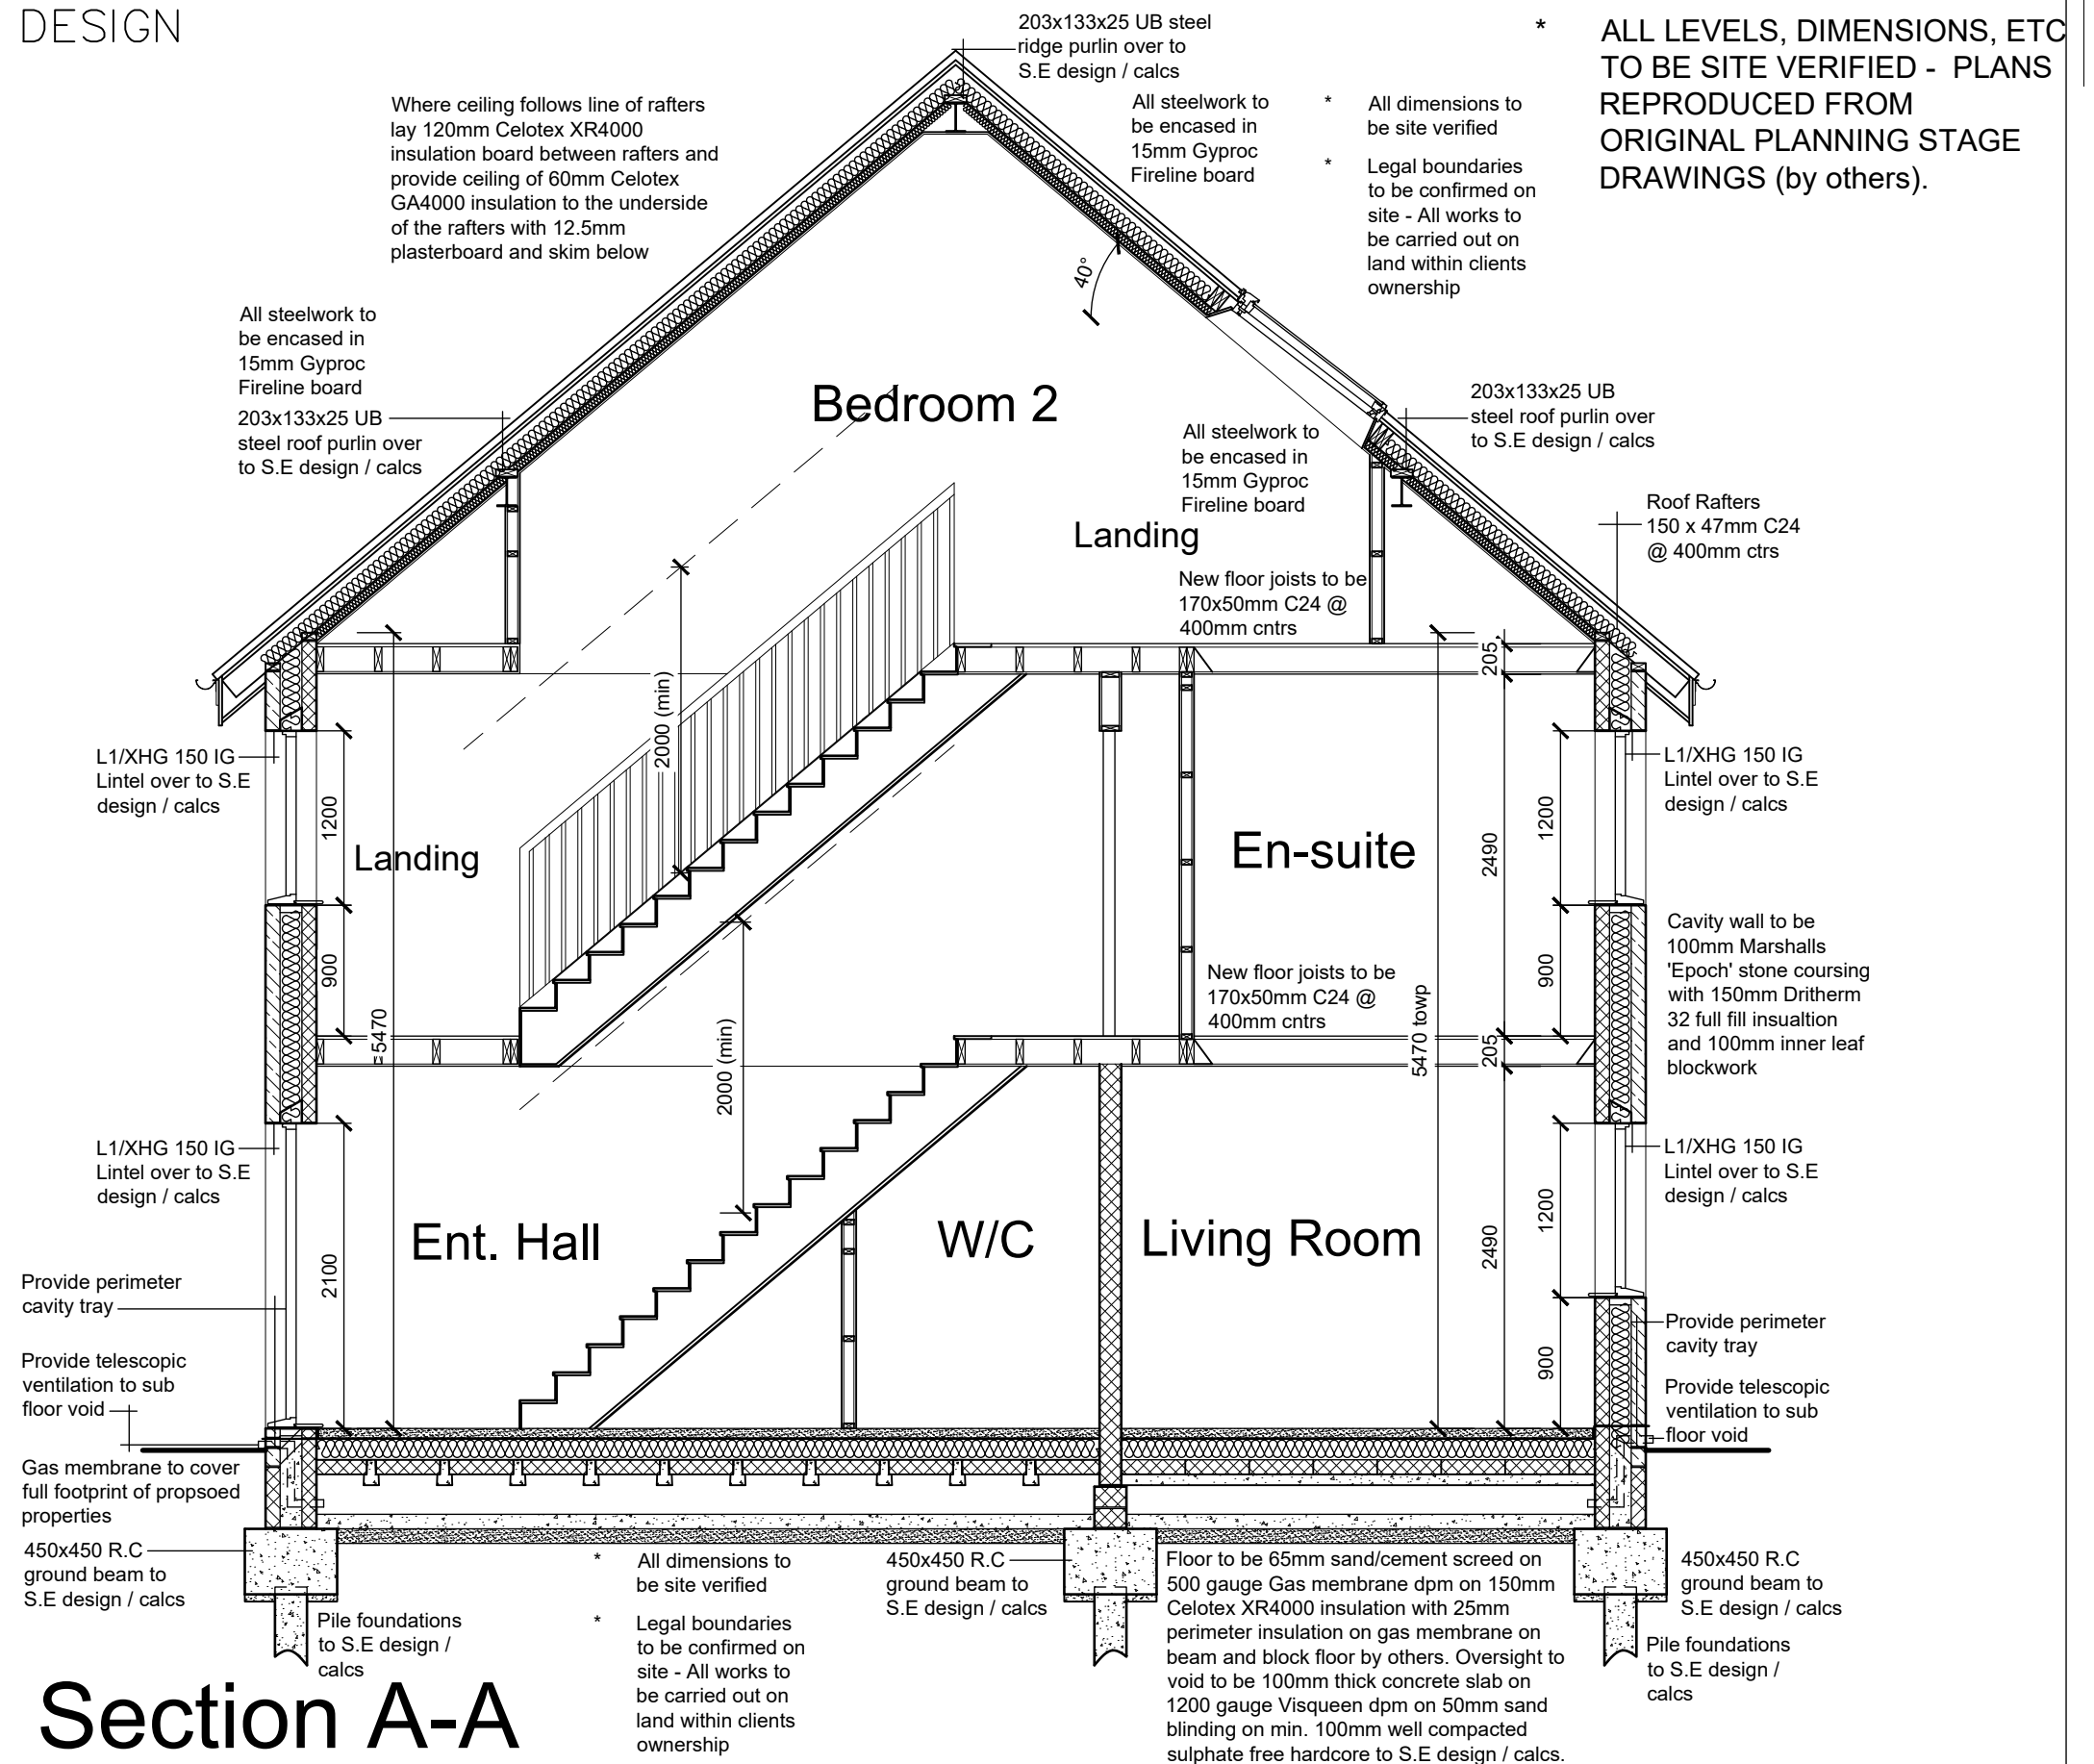

Section A-A

1:50

