
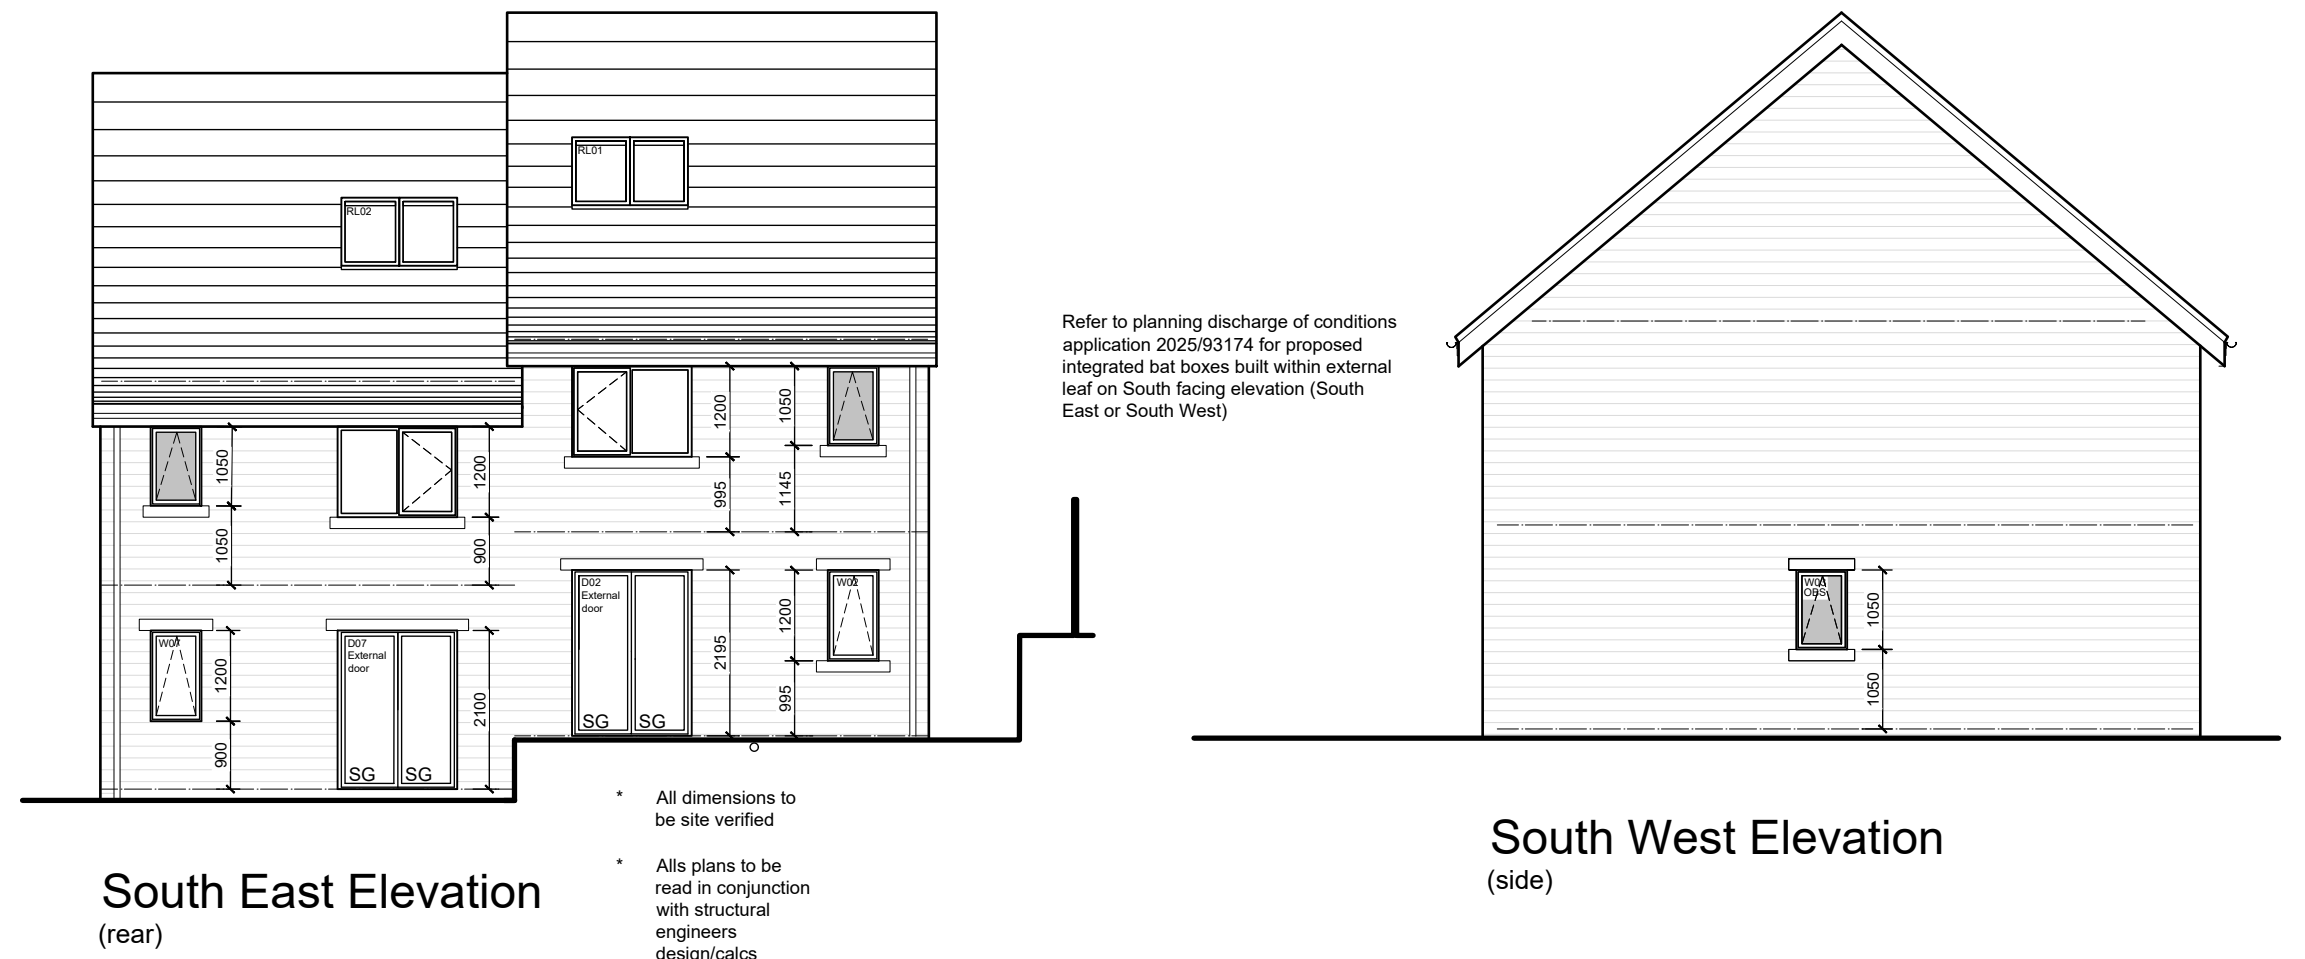


* ALL LEVELS, DIMENSIONS, ETC TO BE SITE VERIFIED -
PLANS REPRODUCED FROM ORIGINAL PLANNING
STAGE DRAWINGS (by others).

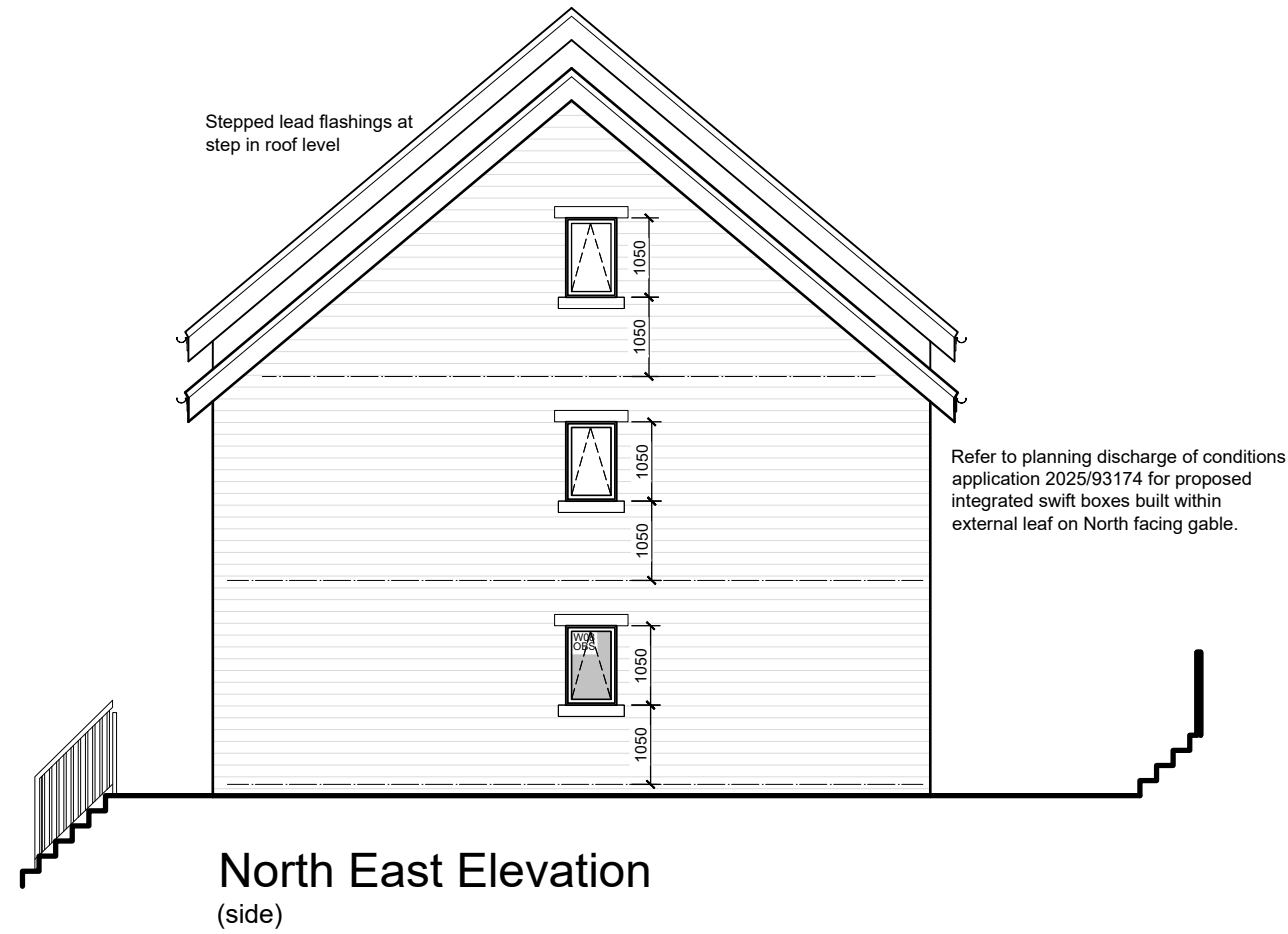

ARCHITECTURE | PLANNING | DESIGN

Malkin Farm
Brow Lane
Holmfirth
HD9 2RJ
07946872499
paul@paulmatthewsarchitectural.co.uk
www.paulmatthewsarchitectural.co.uk

Company Registration Number: 09898149 – Company Registered in England and Wales

Project
Erection of 2 Attached Dwellings on Land Adjacent, 2, Hoyle Ing, Linthwaite, Huddersfield, HD7 5RX.
Client

Walker Good Homes Ltd

Drawing Title/Issue

Building Regulation Stage Elevations

scale 1:100 date 07/2026 sheet size A2 dwg. no. 26/1362/05

KEY

- Ⓢⓓ Smoke alarm ~ mains powered and interconnected
- Ⓢⓓ Heat alarm ~ mains powered and interconnected
- SG Safety Glass
- obs Obscure Glazing
- E Extract Fan
- F Flue
- SVP Soil & Vent pipe
- RWP Rain water pipe
- B.I.G Back inlet gully
- EW Escape Window
- FD30 Fire door
- ⊕ Mechanical Extract Fan

